


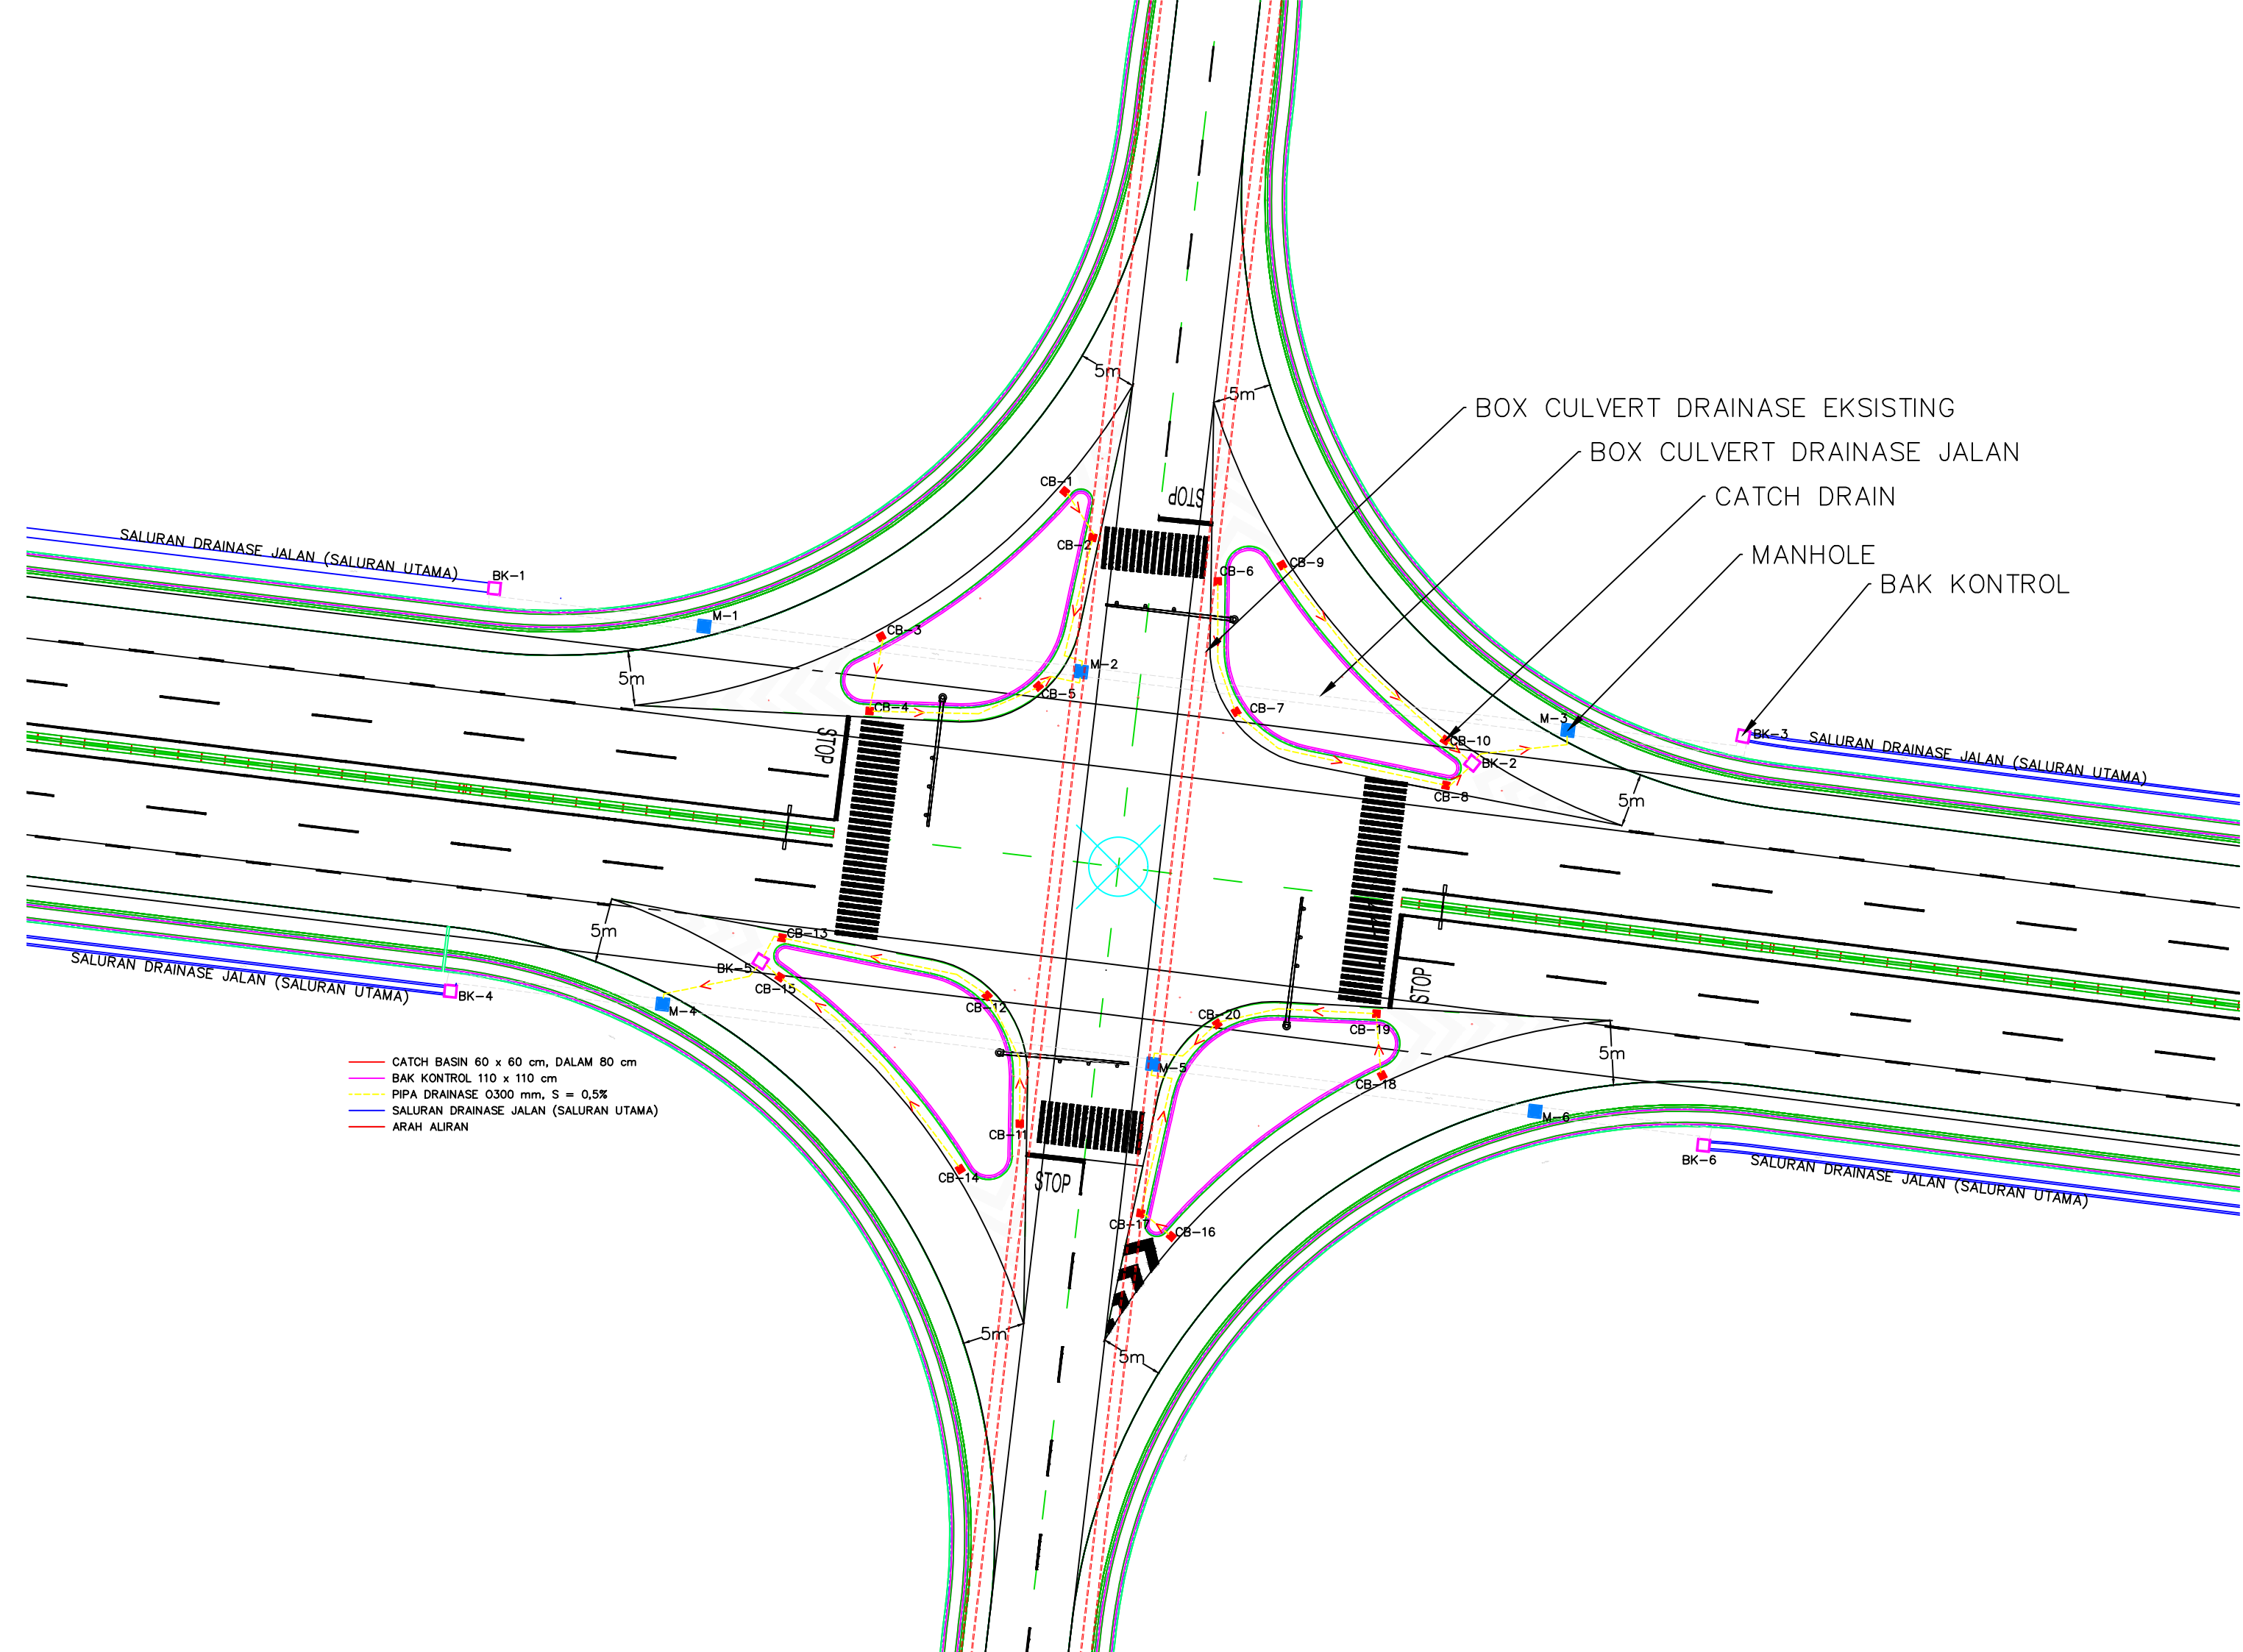

BOX CULVERT DRAINASE EKSISTING

BOX CULVERT DRAINASE JALAN

CATCH DRAIN

MANHOLE

BAK KONTROL

- CATCH BASIN 60 x 60 cm, DALAM 80 cm
- BAK KONTROL 110 x 110 cm
- PIPA DRAINASE Ø300 mm, S = 0,5%
- SALURAN DRAINASE JALAN (SALURAN UTAMA)
- ARAH ALIRAN